SHEET NO : 1 / 2

PROPOSED FACTORY PREMISES ON PLOT NO. 32, SITUATED AT AGRO PROCESSING PARK, BANDAMAILARAM VILLAGE, MULUGU MANDAL, SIDDIPET DISTRICT, TELANGANA STATE.

Belongs to: M/S. IMAGE CROP SCIENCES PRIVATE LIMITED

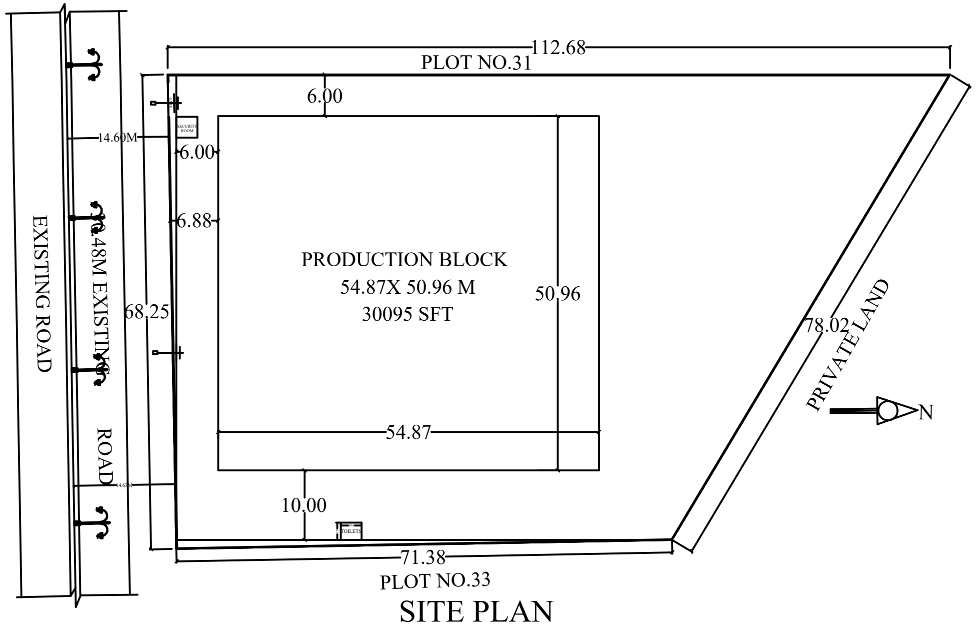
112.68
PLOT NO.31
6.00
14.60M
SECURITY ROOM
6.00
6.88
EXISTING ROAD
0.48M EXISTING ROAD
68.25
PRODUCTION BLOCK
54.87X 50.96 M
30095 SFT
50.96
78.02
PRIVATE LAND
N
54.87
14.63M
10.00
TOILETS
71.38
PLOT NO.33

SITE PLAN
SCALE:1:400

TOTAL PLOT AREA	:	6208.27 SQ MTS
MACHINERY BLOCK AREA	:	2796.00 SQ MTS
SECURITY SHED AREA	:	9.00 SQ MTS
TOILETS SHED AREA	:	7.50 SQ MTS
TOTAL BUILT UP AREA	:	2812.50 SQ MTS

LIST OF MACHINERY

S. NO.	DESCRIPTION	QTY XHP IN NO.S	TOTAL HP
1	REST ROOMS&SECURITY ROOM	1X3.00	3.00
2	WATER PUMP	1X1.00	1.00
		TOTAL : 4 HP	

SIGNATURE OF OCCUPIER

For Image Crop Sciences Pvt. Ltd.,
Authorised Signatory/Director

SIGNATURE OF ARCHITECH/ENGG.

SRI SAI DESIGNERS
ARCHITECTS, ENGINEER'S & CONTRACTOR
T. SRINIVAS Licencee Surveyor, (GHMC)
Licence No, 120/TP10/GHMC/2006
Kamala Nagar, ECIL, HYD-62.
Cell: 9395394670

SHEET NO : 2 / 2

PROPOSED FACTORY PREMISES ON PLOT NO. 32, SITUATED AT AGRO PROCESSING PARK, BANDAMAILARAM VILLAGE, MULUGU MANDAL, SIDDIPET DISTRICT, TELANGANA STATE.

Belongs to: M/S. IMAGE CROP SCIENCES PRIVATE LIMITED

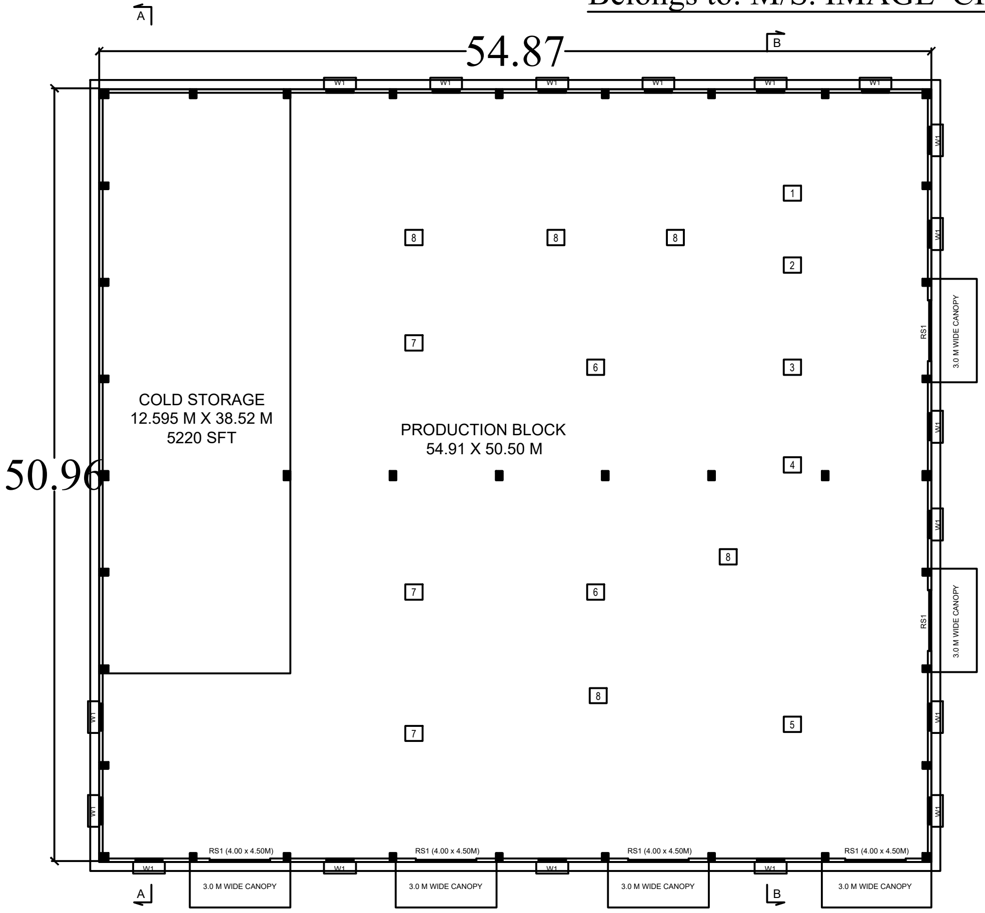
A
B
54.87
50.96
W1
RS1
3.0 M WIDE CANOPY
COLD STORAGE
12.595 M X 38.52 M
5220 SFT
PRODUCTION BLOCK
54.91 X 50.50 M
1
2
3
4
5
6
7
8
RS1 (4.00 x 4.50M)

PRODUCTION BLOCK PLAN

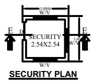
3.0000
W/V
E
D
SECURITY
2.54X2.54
3.00
W/V

SECURITY PLAN

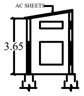
AC SHEETS
3.65

SECTION ON - EE

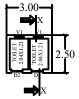
3.00
X
V1
TOILET
2.04X1.21
D2
2.50

TOILETS BLOCK

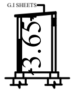
G.I SHEETS
3.65

SECTION ON - XX

LIST OF MACHINERY

S. NO.	DESCRIPTION	QTY XHP IN NO.S	TOTAL HP
1	SEED CLEANER	1X10.00	10.00
2	SEED GRADER	1X10.00	10.00
3	SEED GRAVITY SEPARATOR	1X10.00	10.00
4	SEED TREATMENTS MACHINE	1X15.00	15.00
5	SEED DRYER	1X35.00	35.00
6	AUTO PACKING UNIT	2X5.00	10.00
7	SEED STORAGE BINS	2X2.50	5.00
8	LOW RH REFRIGERATION SYSTEM	5X10.00	50.00
		TOTAL : 145 HP	

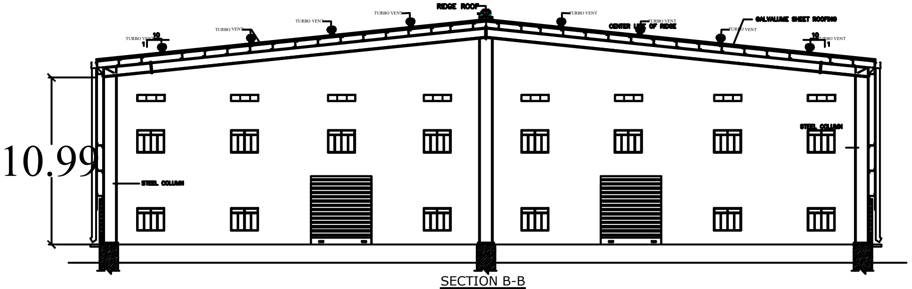
TURBO VENT
RIDGE ROOF
CENTER LINE OF RIDGE
GALVALUME SHEET ROOFING
10
1
10.99
STEEL COLUMN

SECTION B-B

SPECIFICATIONS

FOUNDATION BED : R.C.C
FOUNDATION : UCRS
BASEMENT : CRS
FLOORING : C.C
SUPER STRUCTURE : BRICKS
DOOR &
WINDOWS : M.S

SCHEDULE OF JOINERY

RS	ROLLING SHUTTER	: 3.00X4.00
D	DOOR	: 1.20X2.10
D2	DOOR	: 0.72X2.10
W	WINDOW	: 1.80X1.50
V	VENTILATOR	: 1.80X0.45
V1	VENTILATOR	: 0.60X0.45

SIGNATURE OF OCCUPIER

SIGNATURE OF OCCUPIER

For Image Crop Sciences Pvt. Ltd.
Authorised Signatory/Director

SIGNATURE OF ARCHITECH/ENGG

SRI SAI DESIGNERS
ARCHITECTS, ENGINEER'S & CONTRACTOR
T. SRINIVAS Licencen Surveyor, (GHMC)
Licence No, 120/TP10/GHMC/2006
Kamala Nagar, ECIL, HYD-62.
Cell: 9395394670

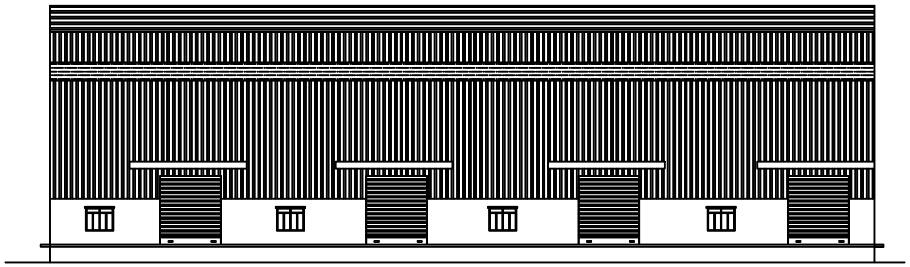

EAST SIDE ELEVATION