
SHEET NO : 1 / 3

PLAN SHOWING THE PROPOSED INDUSTRIAL BUILDING ON PLOT NO:17 , SITUATED AT AGRO PROCESSING PARK,BANDAMAILARAM VILLAGE,MULUGU MANDAL, SIDDIPET DISTRICT, TELANGANA STATE.

Belongs to:M/S.SRI RAMA AGRI GENETICS (INDIA)PRIVATE LIMITED

NOTE : ALL DIMENSIONS ARE IN Meters SCALE : 1 : 100

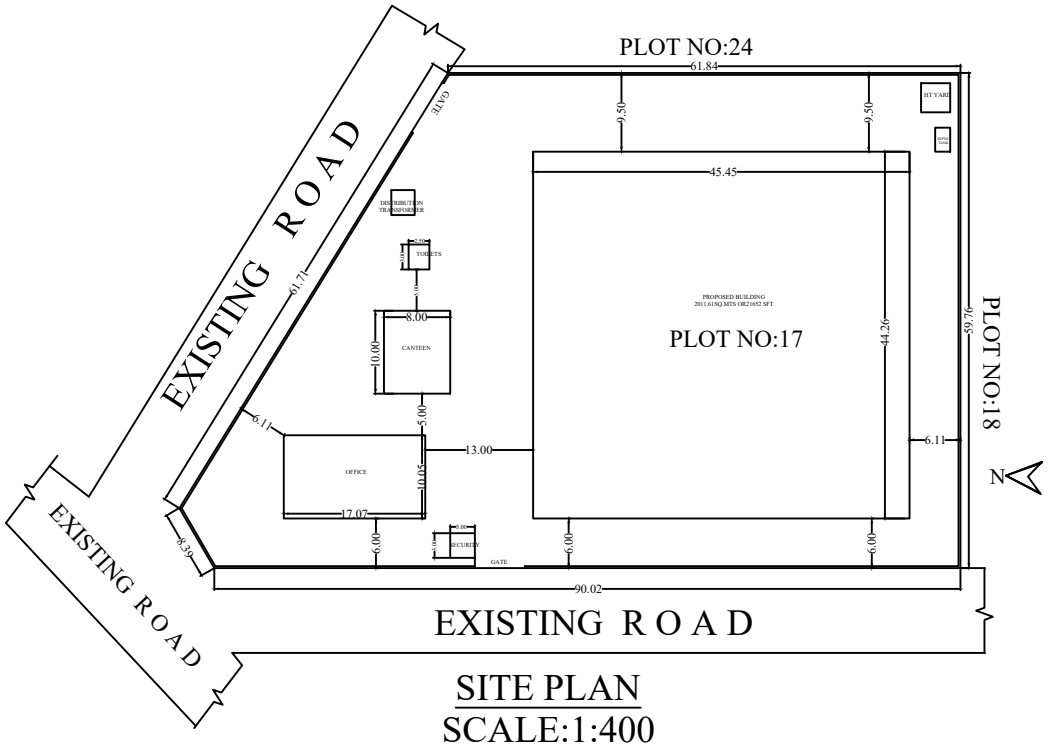

SITE PLAN
SCALE:1:400

TOTAL PLOT AREA	:	4765.83 SQ MTS
MACHINERY BLOCK AREA	:	2011.61 SQ MTS
OFFICE BUILDING AREA	:	171.55 SQ.MTS
CANTEEN BUILDING AREA	:	80.00 SQ.MTS
SECURITY SHED AREA	:	9.00 SQ MTS
TOILETS SHED AREA	:	7.50 SQ MTS
TOTAL BUILT UP AREA	:	2279.66 SQ MTS

LIST OF MACHINERY

S. NO.	DESCRIPTION	QTY XHP IN NO.S	TOTAL HP
1	REST ROOMS&SECURITY ROOM	1X3.00	3.00
2	WATER PUMP	1X2.00	2.00
		TOTAL	: 4 HP

SIGNATURE OF OCCUPIER

For Sri Rama Agri Genetics (India) Pvt. Ltd.
Authorised Signatory / Director


SIGNATURE OF ARCHITECH/ENGG.

SRI SAI DESIGNERS
ARCHITECTS, ENGINEER'S & CONTRACTOR
T. SRINIVAS Licence Surveyor, (GHMC)
Licence No, 120/TP10/GHMC/2006
Kamala Nagar, ECIL, HYD-62.
Cell: 9395394670


PLAN SHOWING THE PROPOSED INDUSTRIAL BUILDING ON PLOT NO:17 , SITUATED AT AGRO PROCESSING PARK,BANDAMAILARAM VILLAGE,MULUGU MANDAL, SIDDIPET DISTRICT, TELANGANA STATE.

Belongs to:M/S.SRI RAMA AGRI GENETICS (INDIA)PRIVATE LIMITED


NOTE : ALL DIMENSIONS ARE IN Meters SCALE : 1 : 100

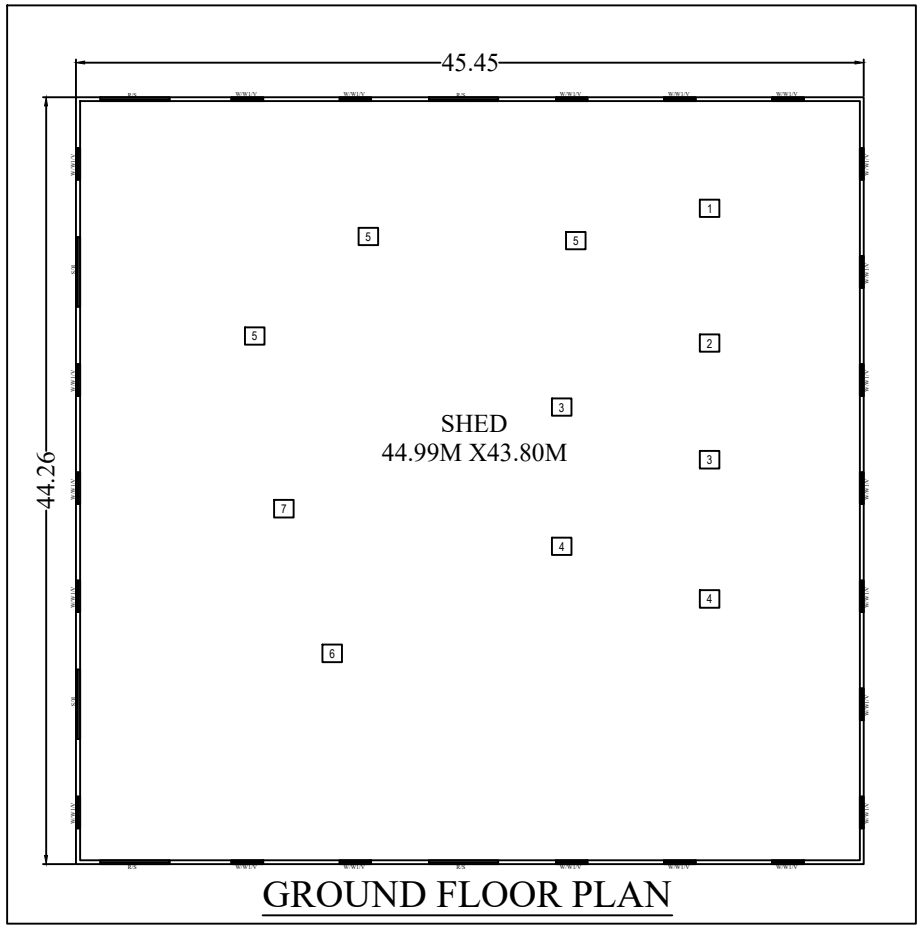


GROUND FLOOR PLAN

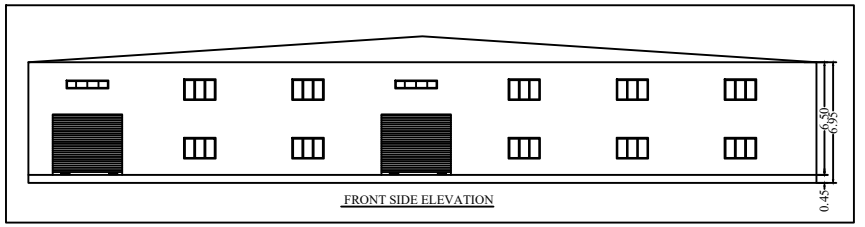


FRONT SIDE ELEVATION

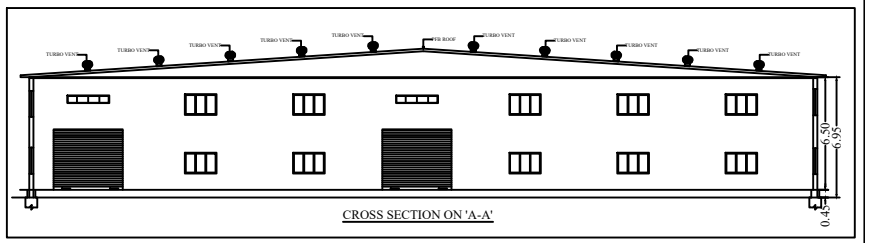

CROSS SECTION ON 'A-A'

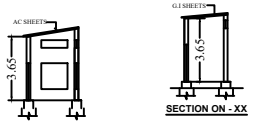


SECTION ON - EE

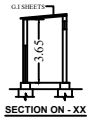

SECTION ON - XX



SECURITY PLAN

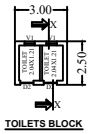

TOILETS BLOCK

LIST OF MACHINERY

S. NO.	DESCRIPTION	QTY 'KHP' IN NO.S	TOTAL HP
1	COLOR COATING MACHINE	1X20.00	20.00
2	BOILER	1X20.00	20.00
3	MACHINE AUTOMATIC PACKING MACHINE	2X5.00	10.00
4	SECONDARY AUTO MACHINE	2X5.00	10.00
5	2 ELEVATORS	4X2.50	10.00
6	AIR COMPRESSOR	1X10.00	10.00
7	LOW BH REFRIGERATION SYSTEM	1X10.00	10.00
		TOTAL :	90 HP

SPECIFICATIONS

FOUNDATION BED	:	R.C.C
FOUNDATION	:	UCRS
BASEMENT	:	CRS
FLOORING	:	C.C
SUPER STRUCTURE	:	BRICKS
DOOR & WINDOWS	:	M.S

SCHEDULE OF JOINERY

RS	ROLLING SHUTTER	: 3.00X4.00
D	DOOR	: 1.20X2.10
D2	DOOR	: 0.72X2.10
W	WINDOW	: 1.80X1.50
V	VENTILATOR	: 1.80X0.45
V1	VENTILATOR	: 0.60X0.45

SIGNATURE OF OCCUPIER

SIGNATURE OF OCCUPIER

For Sri Rama Agri Genetics (India) Pvt. Ltd.
Authorised Signatory / Director

SIGNATURE OF ARCHITECH/ENGG

SRI SAI DESIGNERS
ARCHITECTS, ENGINEER'S & CONTRACTOR
T. SRINIVAS Licencee Surveyor, (GHMC)
Licence No. 120/TP10/GHMC/2008
Kamala Nagar, ELL, HYD-62.
Cell: 9395394573


SHEET NO : 3 / 3

PLAN SHOWING THE PROPOSED INDUSTRIAL BUILDING ON PLOT NO:17 , SITUATED AT AGRO PROCESSING PARK,BANDAMAILARAM VILLAGE,MULUGU MANDAL, SIDDIPET DISTRICT, TELANGANA STATE.


Belongs to:M/S.SRI RAMA AGRI GENETICS (INDIA)PRIVATE LIMITED

NOTE : ALL DIMENSIONS ARE IN Meters SCALE : 1 : 100


CANTEEN

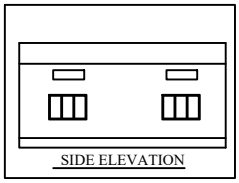


SIDE ELEVATION

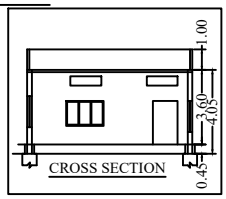

CROSS SECTION

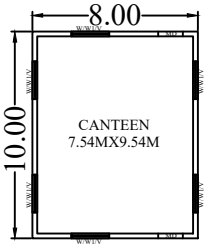

GROUND FLOOR PLAN

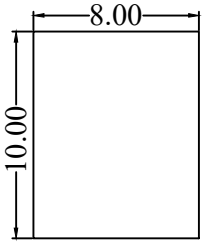

TERRACE FLOOR PLAN

LIST OF MACHINERY			
S. NO.	DESCRIPTION	QTY XHP IN NO.S	TOTAL HP
1	OFFICE BUILDING	1X10.00	10.00
2			
		TOTAL	: 10 HP

SPECIFICATIONS


FOUNDATION BED		: R.C.C
FOUNDATION		: UCRS
BASEMENT		: CRS
FLOORING	: C.C	
SUPER STRUCTURE		: BRICKS
DOOR & WINDOWS		: M.S

SCHEDULE OF JOINERY


RS	ROLLING SHUTTER	: 3.00X4.00
D	DOOR	: 1.20X2.10
D2	DOOR	: 0.72X2.10
W	WINDOW	: 1.80X1.50
V	VENTILATOR	: 1.80X0.45
V1	VENTILATOR	: 0.60X0.45

SIGNATURE OF OCCUPIER

OFFICE

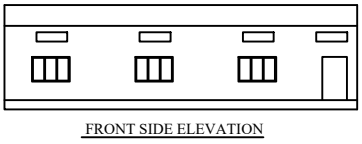


FRONT SIDE ELEVATION

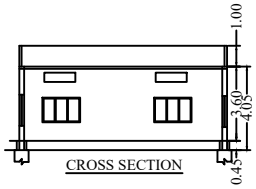


CROSS SECTION

SIGNATURE OF OCCUPIER

For Sri Rama Agri Genetics (India) Pvt. Ltd.
Authorised Signatory / Director

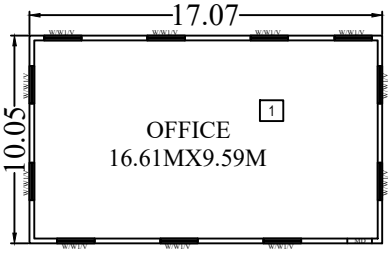

GROUND FLOOR PLAN

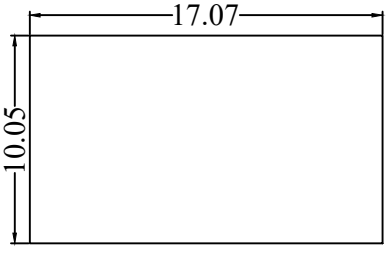

TERRACE FLOOR PLAN

SIGNATURE OF ARCHITECH/ENGG.

SRI SAI DESIGNERS
ARCHITECTS, ENGINEER'S & CONTRACTOR
T. SRINIVAS Licencee Surveyor, (GHMC)
Licence No. 120/TP(O)/GHMC/2008
Kamala Nagar, ECIL, HYD-62.
Cell: 9395391670