GOVERNMENT OF TELANGANA

FACTORIES DEPARTMENT

From
Joint Chief Inspector of Factories
Block No: 304, 3rd Floor,Maitrivihar Comercial Complex,Besides Passport Office (Aditya Trade Center)Ameerpet, Hyderabad - 500038

To
The Occupier
East Pharma Technologies
Galaxy Floor
No21,,Rayadurga
Panmaktha,Hitechcity,RAID URG
PANMAKTHA,Serilingampally,Rangareddy,500032

D.Dis.A6/MBNR/3100/2024, Dated: 24/02/2025

Sir,

Sub: Factories Act, 1948 - Plans of East Pharma Technologies, Door No: 51,52 & 53, Sy No-408 to 412 and 418 to 452 to 459435, Jadcherla, Jadcherla(V), Jadcherla(M), Mahbubnagar(D) - 509301 , Approved Regarding.


Ref: MED0070019138126

* * *


Plans of the factory received in the reference cited are approved under Factories Act 1948 for 1310HP subject to following conditions: 1. Air handling unit with air changes as per National Building Code shall be provided to all areas in the machinery hall where persons are employed 2. Each room shall be provided with two exits 3. Fire prevention and control measures shall be taken as per Section 38 and Rule 61 of Factories Act and Rules made thereunder 4. One more door shall be provided for Admin Block

Note:


1) In respect of new factories manufacturing activity shall not be commenced unless a notice of occupation (License application in Form No: 2) accompanied by challan for requisite fee, etc., are submitted under Section 7 read with rule 4 (1) & (6) to the Inspector of Factories concerned.
2) This is a digitally signed certificate and does not require physical signature. This certificate can be verified at https://tgfactories.cgg.gov.in/ by furnishing the registration certificate number mentioned in the certificate.

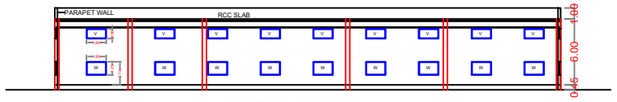


SECTION AT "B-B"

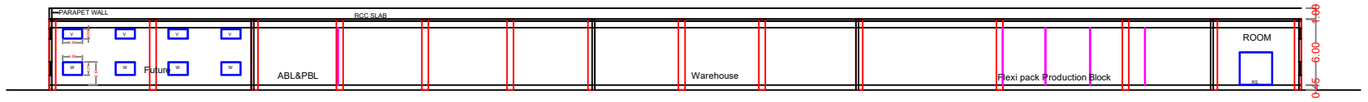


SECTION AT "A-A"

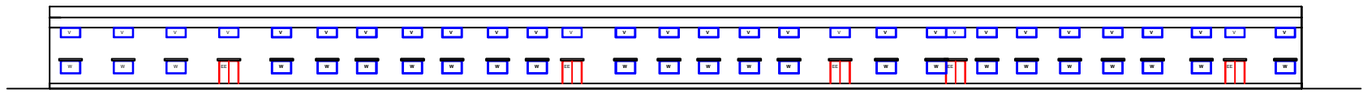


ELEVATION

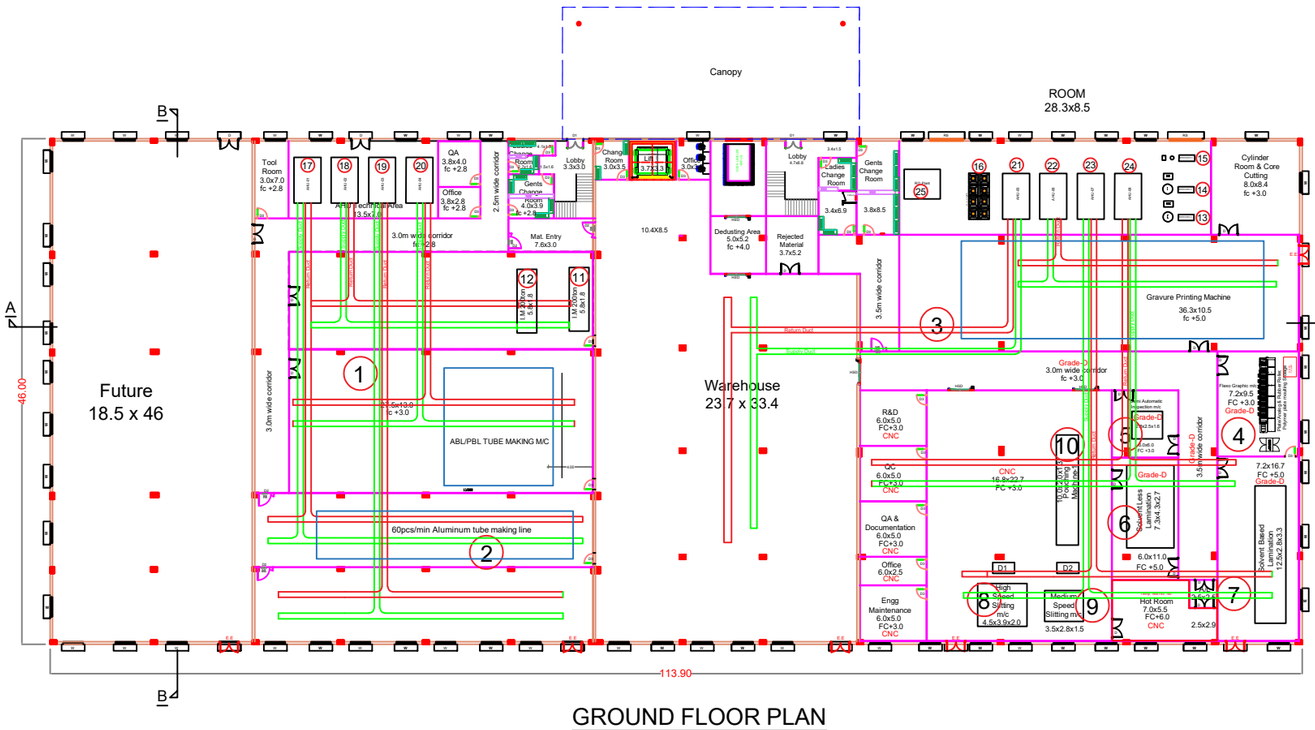


GROUND FLOOR PLAN

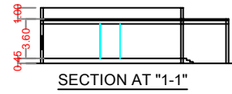


SECTION AT "1-1"

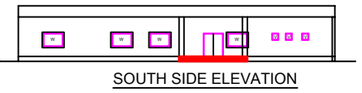


SOUTH SIDE ELEVATION

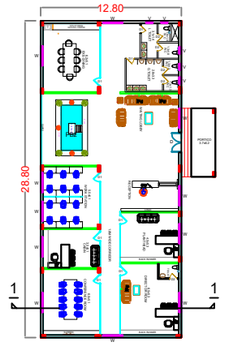


GROUND FLOOR PLAN
ADMIN BLOCK

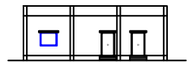


EAST SIDE ELEVATION

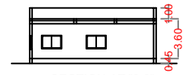

SECTION AT "2-2"

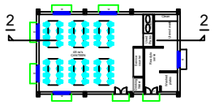

GROUND FLOOR PLAN
CANTEEN

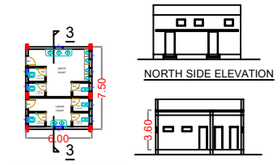


NORTH SIDE ELEVATION

GROUND FLOOR PLAN
TOILET BLOCK


SECTION AT "3-3"




ELEVATION SECTION AT "4-4"

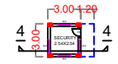

GROUND FLOOR PLAN
SECURITY

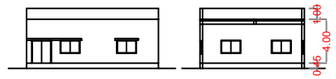

ELEVATION SECTION AT "5-5"

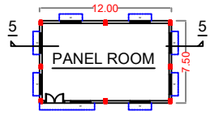

GROUND FLOOR PLAN

List of Equipments

S.No	Type	Peak load In kw	Dimensions in MM L*W*H	Remarks
1	ABL /PBL Tube making Machine	56.4	17200*10000*4000	
2	Collopsible Aluminium Tube Making Machine	128	26000*3629*4252.4	
3	Gravure printing Machine	431	30500*5900*500	
4	Flexo Printing Machine	60	6790*1540*2275	
5	Inspection Machine	15	2775*2509*1640	
6	Solvent less Lamination Machine	58	7300*4350*2750	
7	Solvent base Lamination Machine	93	12500*2800*3300	
8	High speed slitting Machine	11	4496*3977*1920	
9	Horizontal slitting Machine	35	3510*2800*1450	
10	Pouching Machine	15.4	10058*1829*1524	
11	Moulding Machine	33.6	5500*1800*2000	
12	Moulding Machine	33.6	5800*1800*2100	
13	Air compressor 180 Cfm-8 Bar with Dryer &Air Receiver Tank	26	3250*2130*1500	
14	Air compressor 180 Cfm-8 Bar with Dryer &Air Receiver Tank	26	3250*2130*1500	
15	Air compressor 10Cfm,16-20 Bar with Dryer &Air Receiver Tank	5	3000*1200*1000	
16	Chiller 250 TR	220	-	
17	AHU 01	5	-	
18	AHU 02	11.7	-	
19	AHU 03	5	-	
20	AHU 04	7.5	-	
21	AHU 05	11.7	-	
22	AHU 06	7.5	-	
23	AHU 07	5	-	
24	AHU 08	5	-	
25	Ro Plant	5	-	
		1310.4		

Supply Duct Routing

Return Duct Routing

PLAN SHOWING THE PROPOSED BUILDINGS OF M/S EAST PHARMA TECHNOLOGIES, UNIT-3, PLOT NO.51,52&53, IN SY NOS.408 TO 412 & 452 TO 459, SITUATED AT GREEN INDUSTRIAL PARK, POLEPALLE (V),JADCHERLA (MANDAL), MAHBOOBNAGAR DIST,TELANGANA -509302

SPECIFICATIONS		
FOOTINGS	:	R.C.C M25
BASEMENT	:	C.R.S
WALL	:	BRICK WALL
PLASTERING	:	IN C.M 1:6
DORRS&WINDOWS	:	ALUMINUM
FLOORING	:	VDF
LINTELS,CHAJJAS	:	R.C.C M25
COLUMNS,BEAMS,SLAB	:	R.C.C M25
ROOF	:	R.C.C M25

AREAS

PRODUCTION BLOCK
GROUND FLOOR AREA : 5240.00 SQM

SECURITY BLOCK
GROUND FLOOR AREA : 9.00 SQM

ADMIN BLOCK
GROUND FLOOR AREA : 369.00 SQM

CANTEEN BLOCK
GROUND FLOOR AREA : 98.00 SQM

TOILET BLOCK
GROUND FLOOR AREA : 45.00 SQM

UTILITY BLOCK
GROUND FLOOR AREA : 90.00 SQM

SCHEDULE OPENINGS

DOORS:- D 1800X2100
D1 1500X2100
D2 1500X2100
D3 1000X2100
D4 750X2100

WINDOWS:- W 1800X1200
W1 1500X1200
W2 1200X1200

VENTILATORS:- V 1800X900
V1 900X450

ROLLING SHUTTER :- RS 3000X3000

EMERGENCY EXIT:- EE 1800X2100
HSD 2400X2100

OWNER'S SIGNATURE

K.PRABHAKAR REDDY.
STRUCTURAL ENGINEER.
G.H.M.C LICENCE NO.366

ALL DIMENSIONS ARE IN MTS&MM


NORTH


PROPOSED
EXISTING
TO BE DISMANTLED

SCALE	1 : 100		
DRAWN	V.L.N	DRG NO.	EP-2

KSA CONSULTANTS PRIVATE LIMITED

33,PANCOM CHAMBERS
RAJ BHAVAN ROAD,
SOMAJIGUDA, HYDERABAD - 5
PH : 2331 0599,

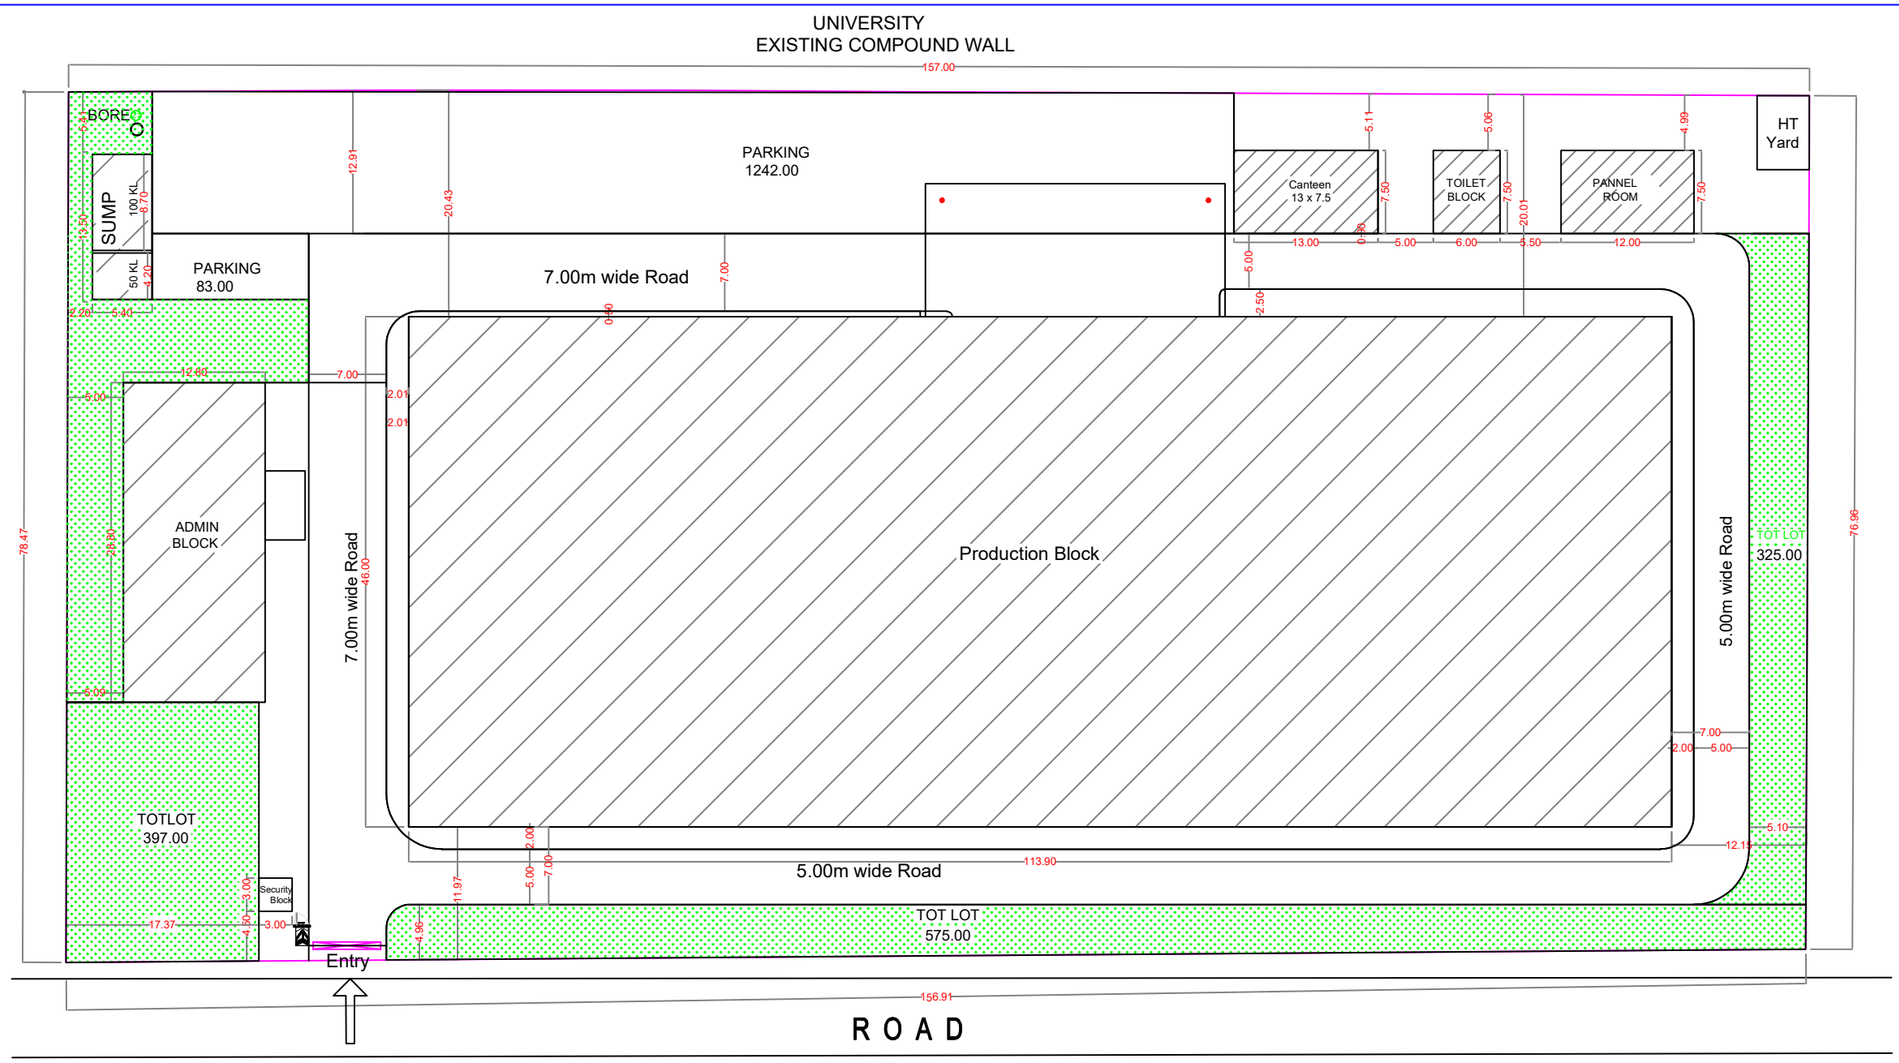

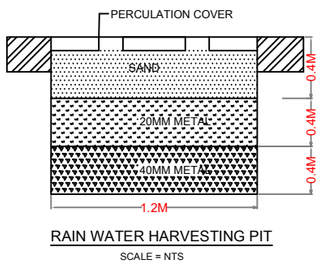

RAIN WATER HARVESTING PIT

SCALE = NTS

S.NO.	DESCRIPTION	L IN MTS	B IN MTS	D/H IN MTS	AREA IN SQ.M
1.	PRODUCTION BLOCK GROUND FLOOR	113.90	46.00	6.00	5240.00
2.	SUMP&FIRE HYDRANT SUMP	13.50	5.40	3.00	73.00
3.	SECURITY	3.00	3.00	3.60	9.00
4.	ADMIN BLOCK	12.80	28.80	3.60	369.00
5.	CANTEEN	13.00	7.50	3.60	98.00
6.	TOILET BLOCK	6.00	7.50	3.00	45.00
7.	PANNEL ROOM	12.00	7.50	4.00	90.00
				TOTAL BUILTUP AREA	5924.00 SQM

TOTAL PLOT AREA : 12219.00 SQM

TOT LOT AREA REQUIRED 10% : 1222.00 SQM
TOT LOT AREA PROVIDED : 1297.00 SQM

TOTAL BUILTUP AREA : 5924.00 SQM

PARKING AREA REQUIRED 22% : 1304.00 SQM
PARKING AREA PROVIDED : 1325.00 SQM

ALL DIMENSIONS ARE IN MTS &MM

PROPOSED
EXISTING
TO BE DISMANTILE

NORTH

N

SITE PLAN SHOWING THE PROPOSED BUILDINGS
OF M/S EAST PHARMA TECHNOLOGIES, UNIT-3,
PLOT NO.51,52&53,
IN SY NOS.408 TO 412 & 452 TO 459, SITUATED AT
GREEN INDUSTRIAL PARK,
POLEPALLE (V),JADCHERLA (MANDAL),
MAHBOOBNAGAR DIST,TELANGANA -509302

OWNER'S SIGNATURE

K.PRABHAKAR REDDY.
STRUCTURAL ENGINEER,
G.H.M.C LICENCE NO.366

SCALE	1 : 400		
DRAWN	V.L.N	DRG NO.	EP-1

KSA CONSULTANTS PRIVATE LIMITED
33, PANCOM CHAMBERS, RAJ BHAVAN ROAD, SOMAJIGUDA, HYDERABAD - 82.
PH. : 2331 0559,